


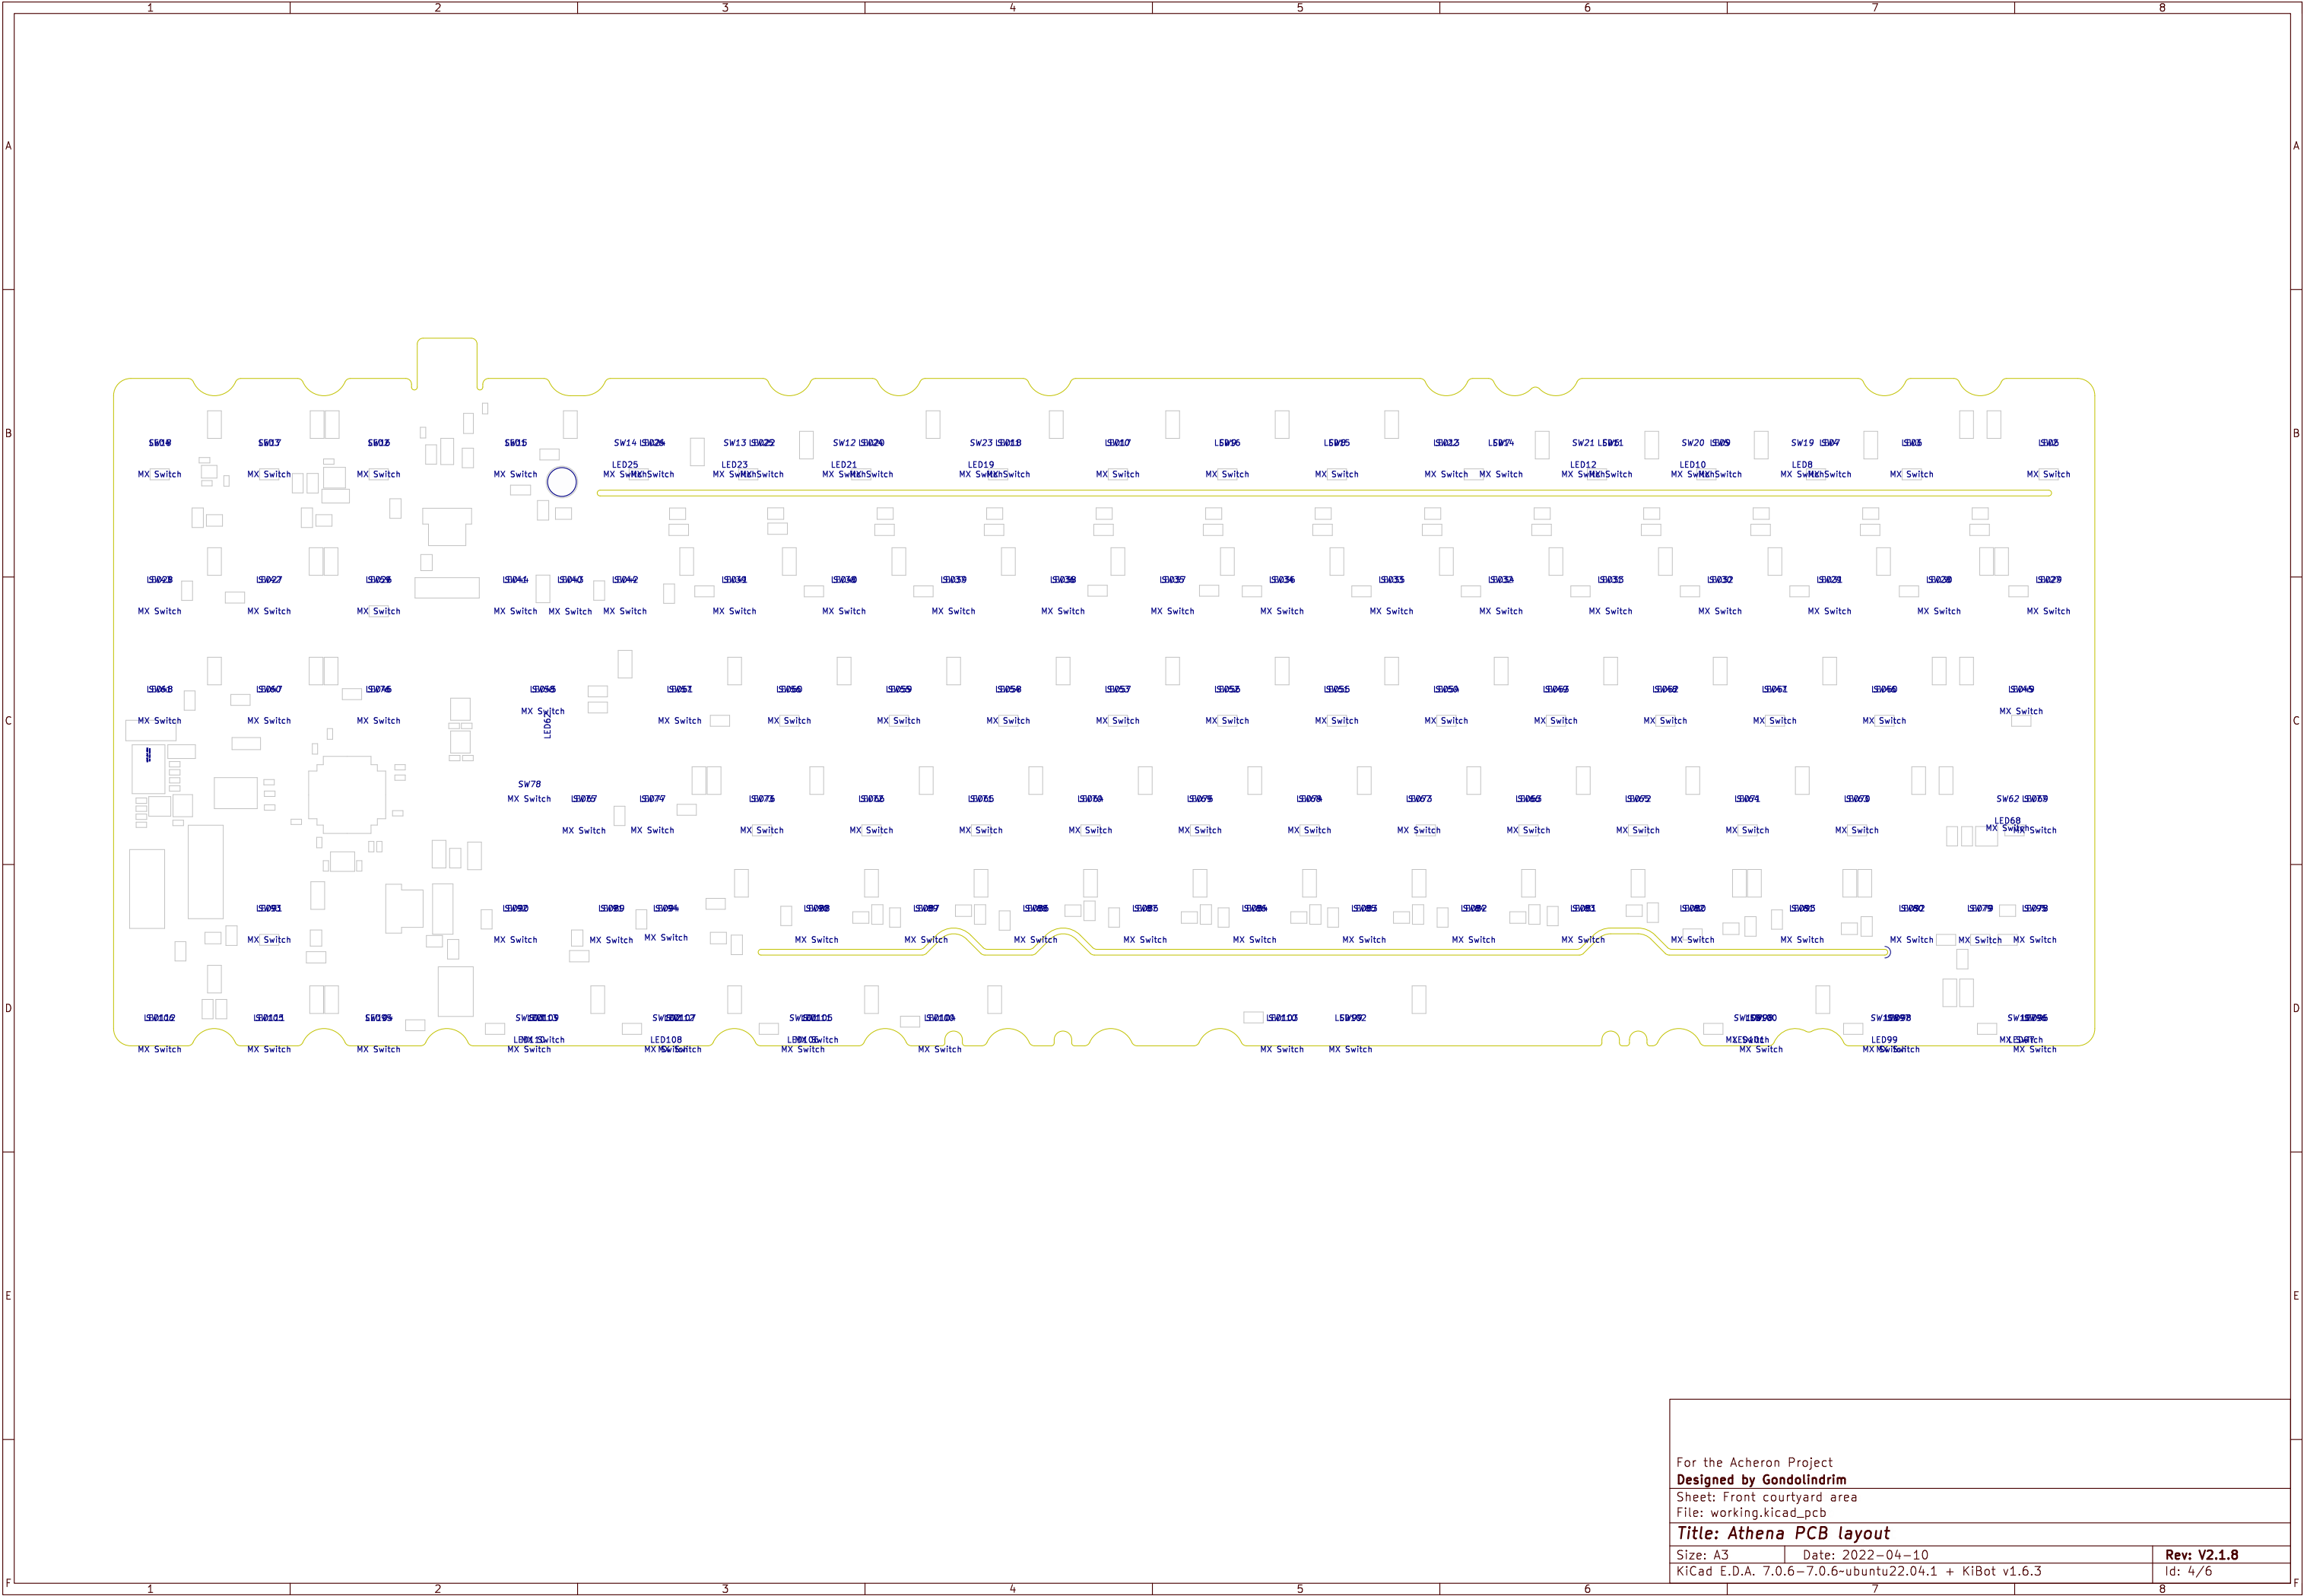

For the Acheron Project		
Designed by Gondolindrim		
Sheet: Front courtyard area		
File: working.kicad_pcb		
Title: Athena PCB layout		
Size: A3	Date: 2022-04-10	Rev: V2.1.8
KiCad E.D.A. 7.0.6-7.0.6-ubuntu22.04.1 + KiBot v1.6.3		Id: 4/6